


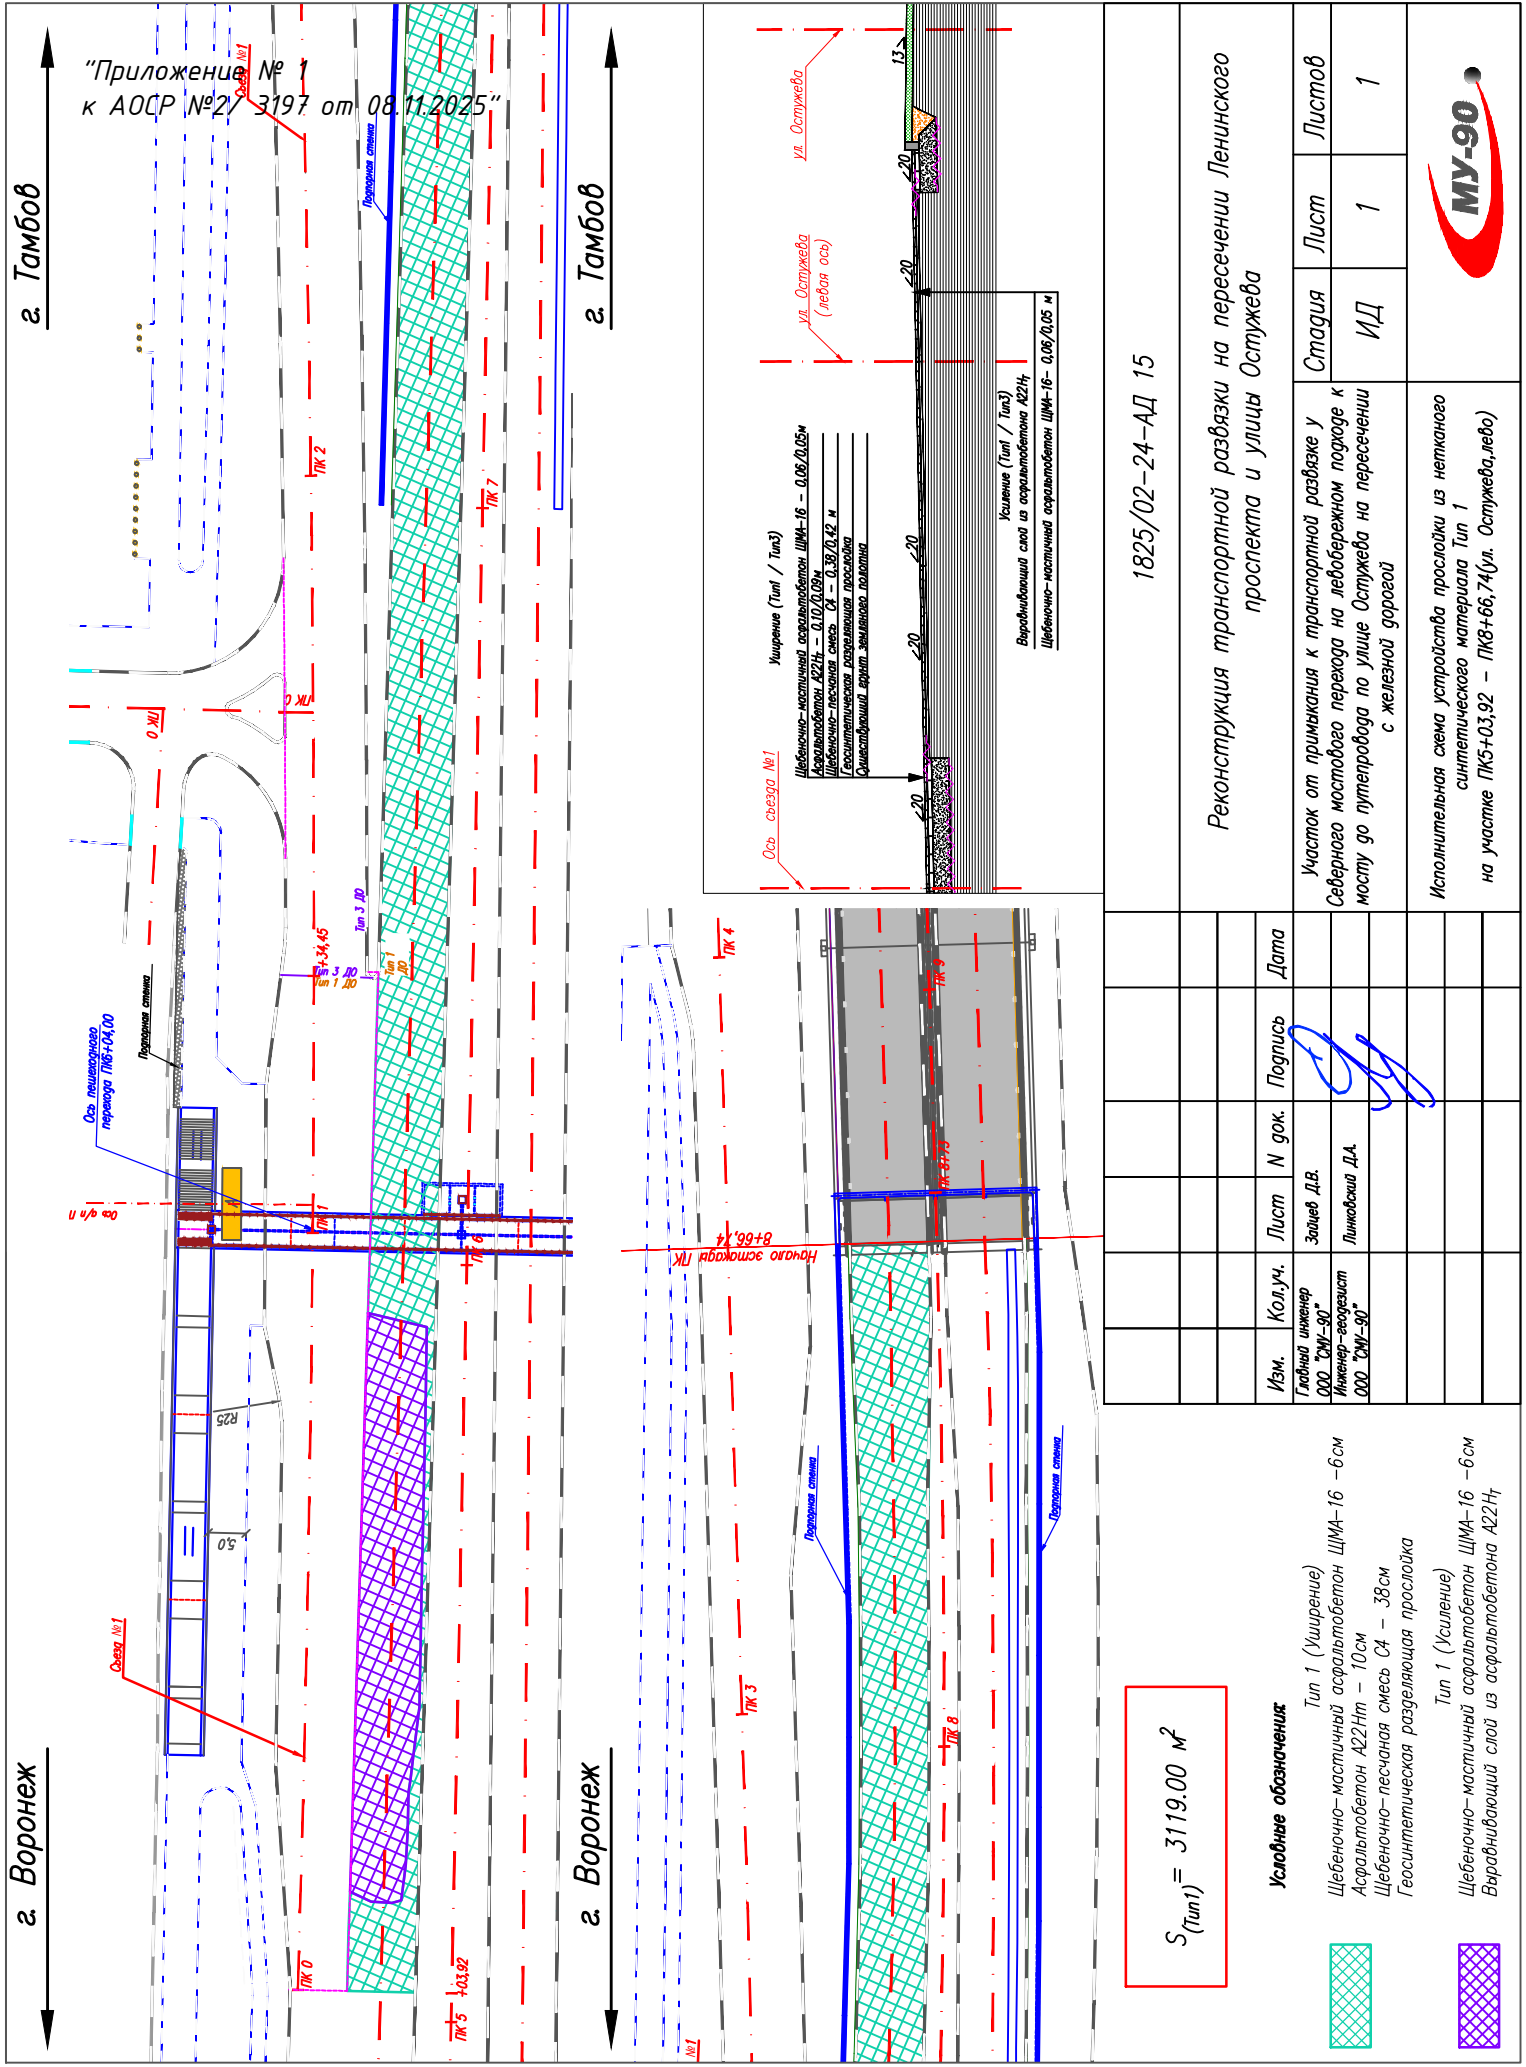

"Приложение № 1
к АОСР №27/3197 от 08.11.2025"

а Воронеж

а Воронеж

а Тамбов


$S_{(Тит1)} = 3119.00 \text{ м}^2$

Условные обозначения

- Тип 1 (Уширение)
Щебеночно-мастичный асфальтобетон ШМА-16 - 6см
Асфальтобетон А22Нт - 10см
Щебеночно-песчаная смесь С4 - 38см
Геосинтетическая разделяющая прослойка
- Тип 1 (Усиление)
Щебеночно-мастичный асфальтобетон ШМА-16 - 6см
Выровнивающий слой из асфальтобетона А22Нт

1825/02-24-АД 15

Реконструкция транспортной развязки на пересечении Ленинского проспекта и улицы Остужева

 Глобальный инженер ООО "МУ-90"	Зайцев Д.В.		Участок от примыкания к транспортной развязке у Северного мостового перехода на левобережном подходе к мосту до путепровода по улице Остужева на пересечении с железной дорогой	Стация	Лист	Листов
Инженер-геодезист ООО "МУ-90"	Линавский Д.А.			ИД	1	1
			Исполнительная схема устройства прослойки из нетканого синтетического материала Тип 1 на участке ПК5+03.92 – ПК8+66,74(ул. Остужева, лево)	